


Frame: L24

Plan: PK4-GF-LBW-70.075
Length: 3.232 m Height: 2.615 m Weight: 42.0 kg

Project: HG260017#1-1 LOT 925 LOT 925 (42)
Job: HG260017 Date: 2026-03-05
STUNNING CRESCENT NARANGBA

HYTEK

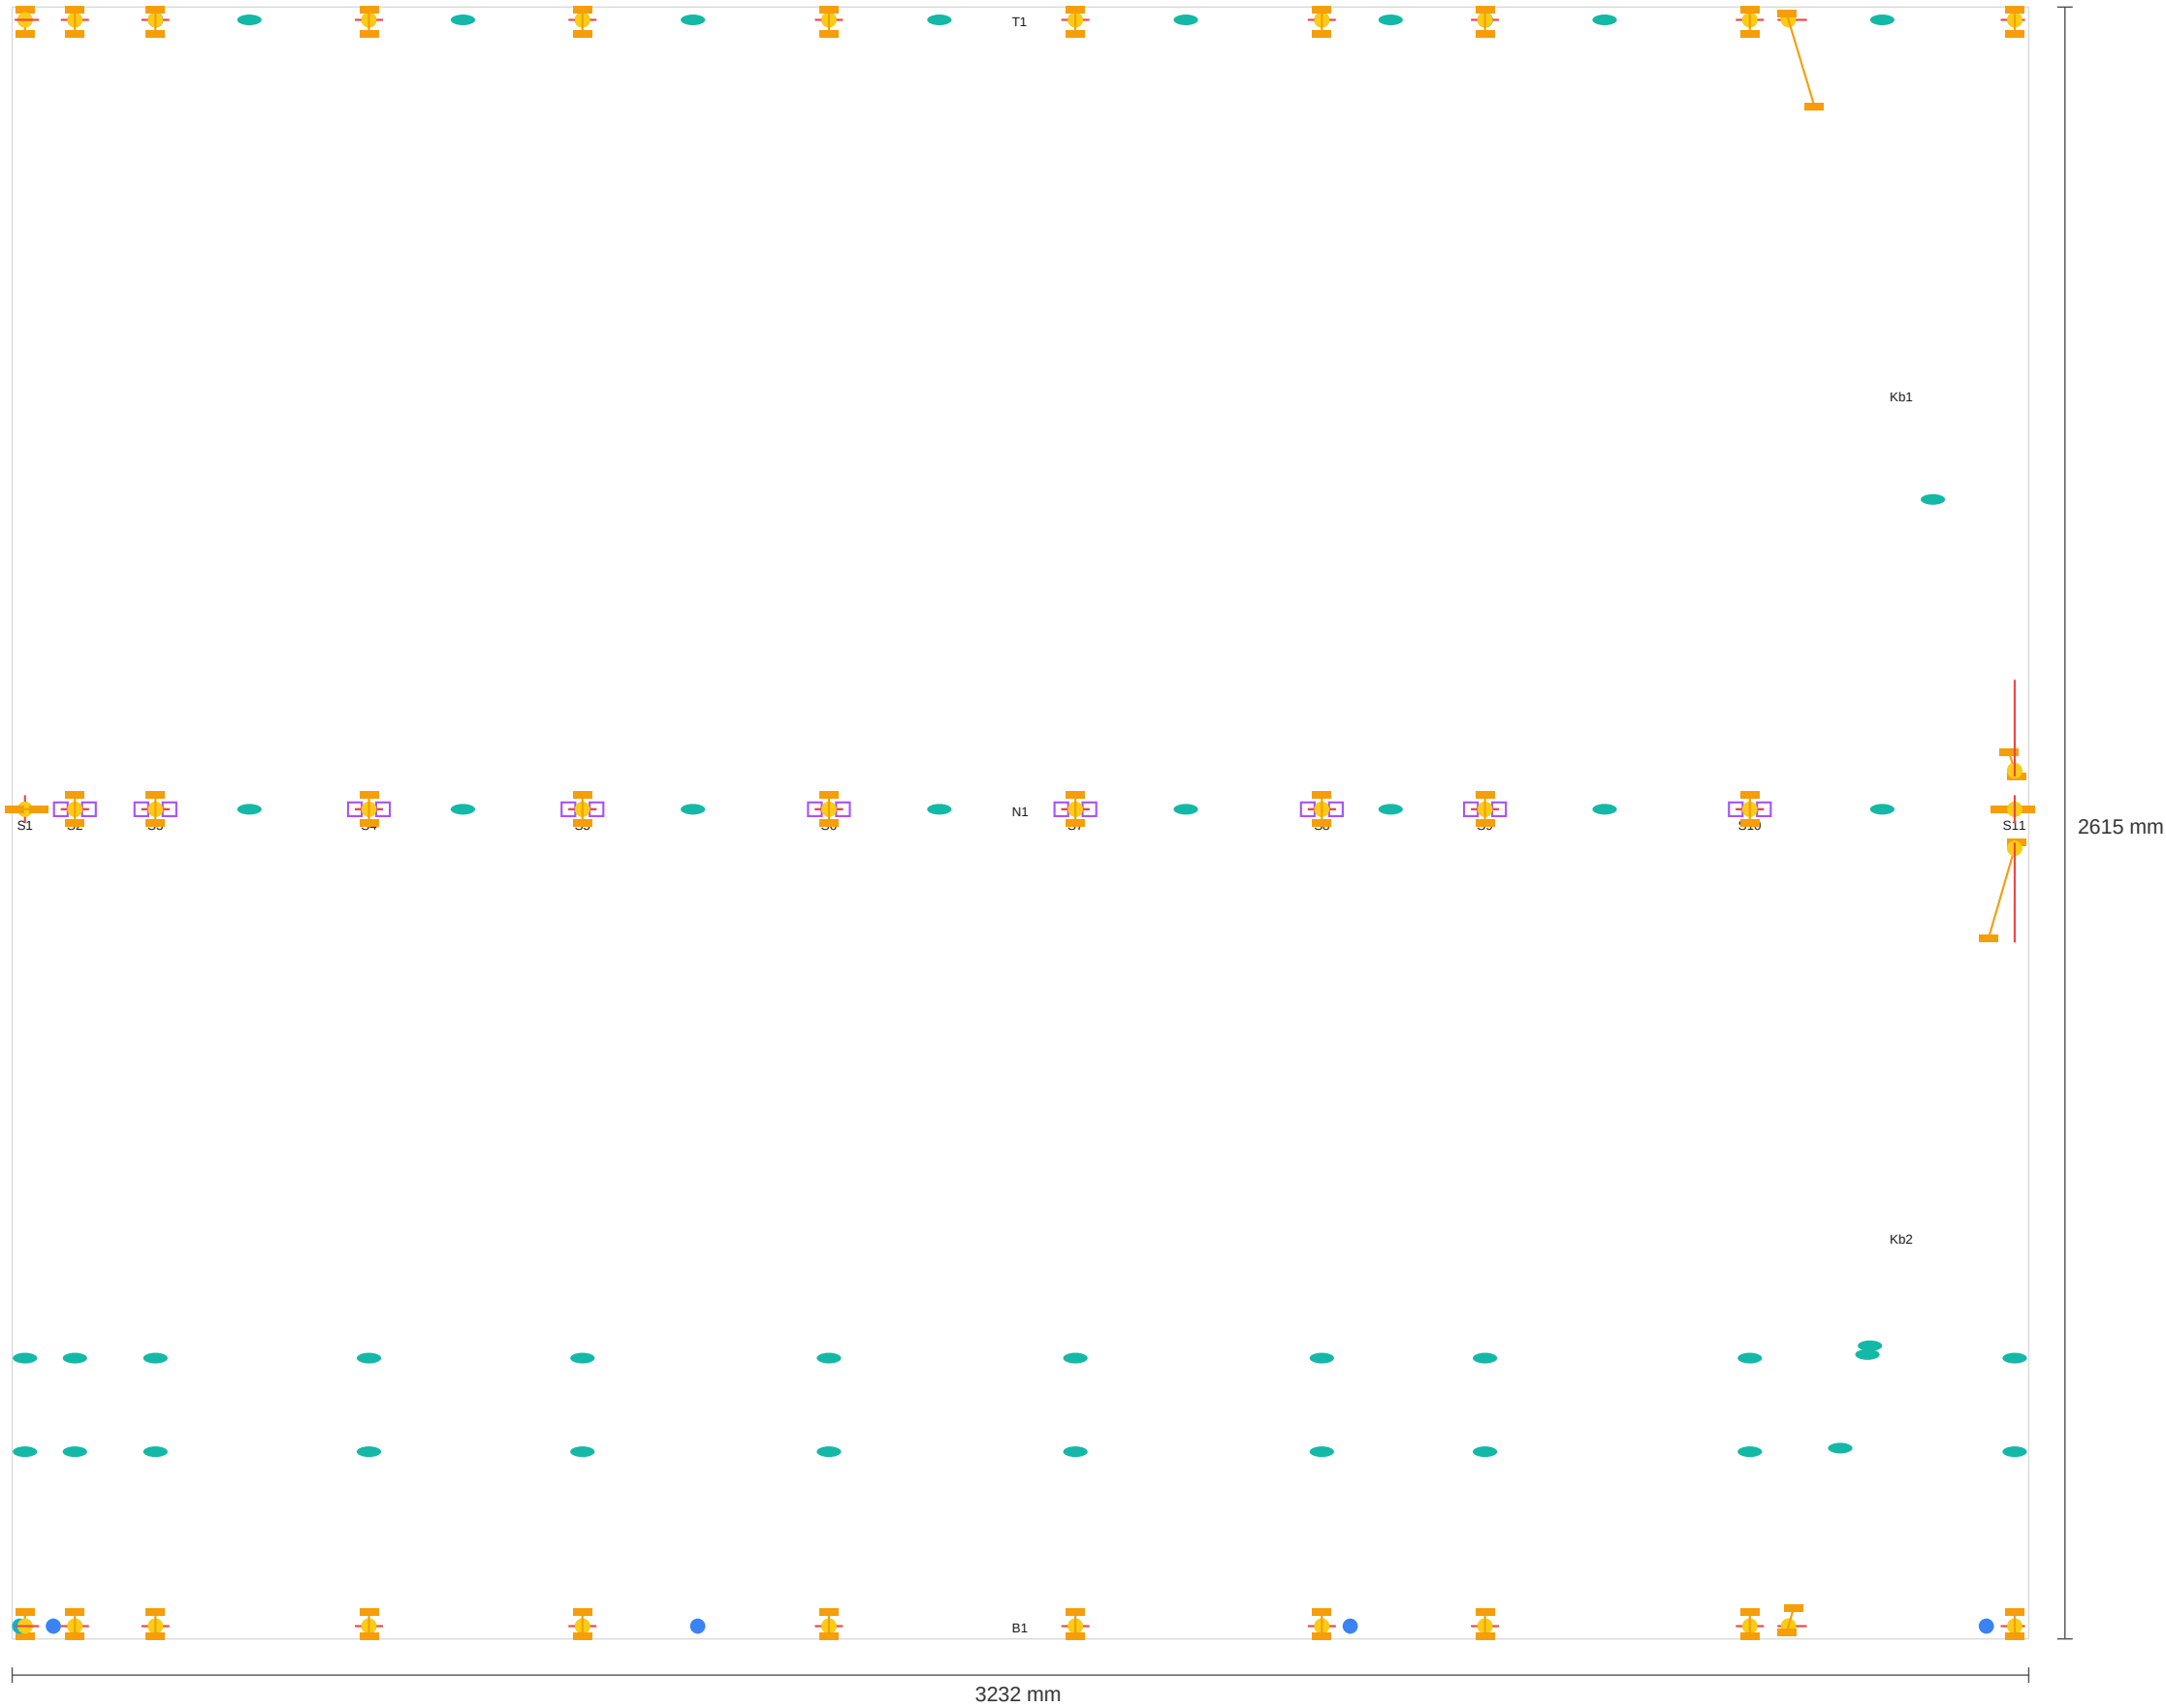


Frame: L29

Plan: PK4-GF-LBW-70.075
Length: 2.010 m Height: 2.615 m Weight: 27.5 kg

Project: HG260017#1-1 LOT 925 LOT 925 (42)
Job: HG260017 Date: 2026-03-05
STUNNING CRESCENT NARANGBA

HYTEK

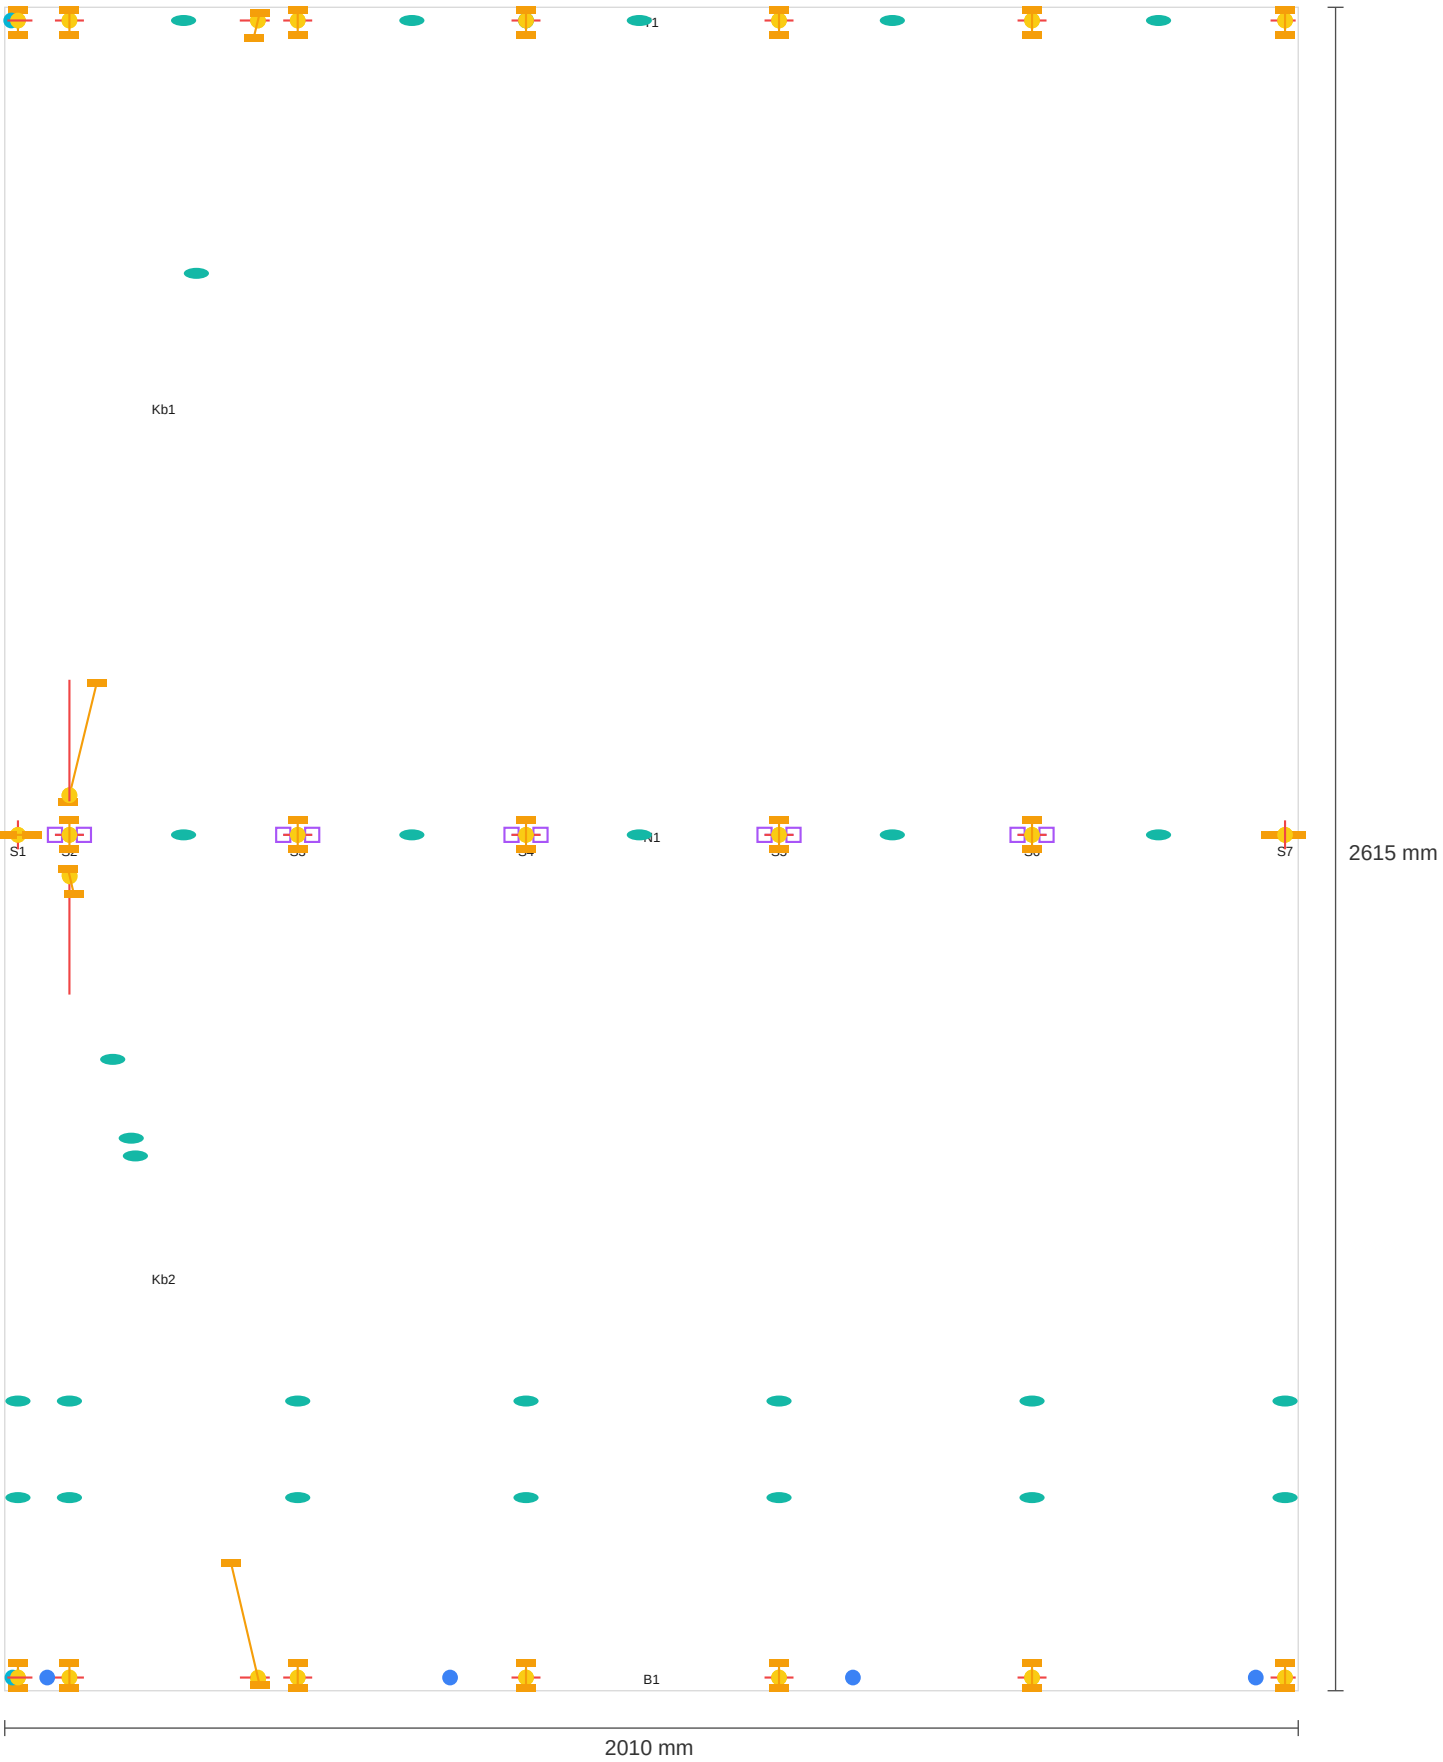


Frame: L27

Plan: PK4-GF-LBW-70.075
Length: 1.960 m Height: 2.615 m Weight: 33.8 kg

Project: HG260017#1-1 LOT 925 LOT 925 (42)
Job: HG260017 Date: 2026-03-05
STUNNING CRESCENT NARANGBA

HYTEK

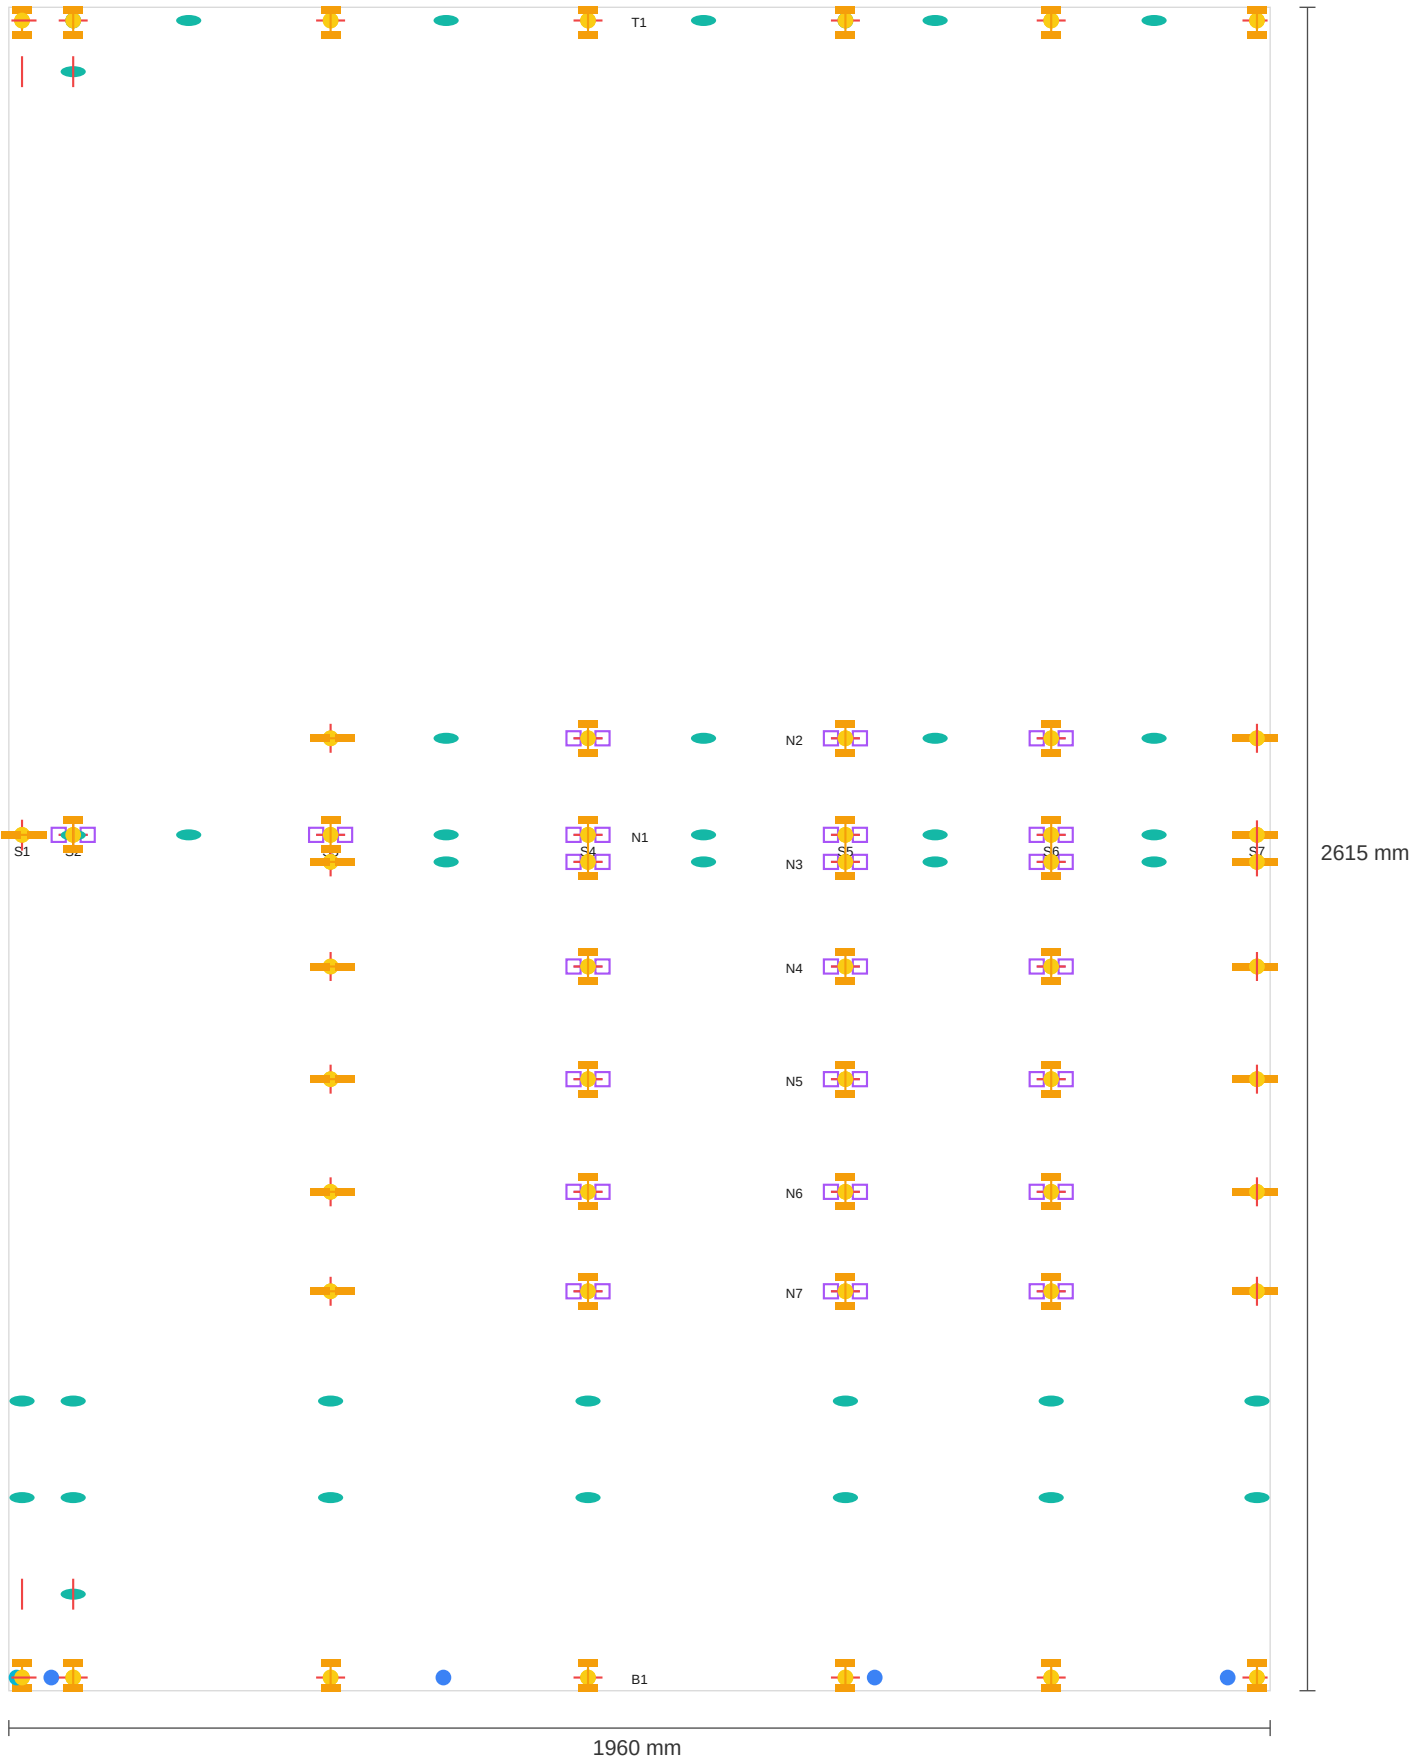


Frame: L30

Plan: PK4-GF-LBW-70.075
Length: 3.590 m Height: 2.615 m Weight: 53.3 kg

Project: HG260017#1-1 LOT 925 LOT 925 (42)
Job: HG260017 Date: 2026-03-05
STUNNING CRESCENT NARANGBA


HYTEK

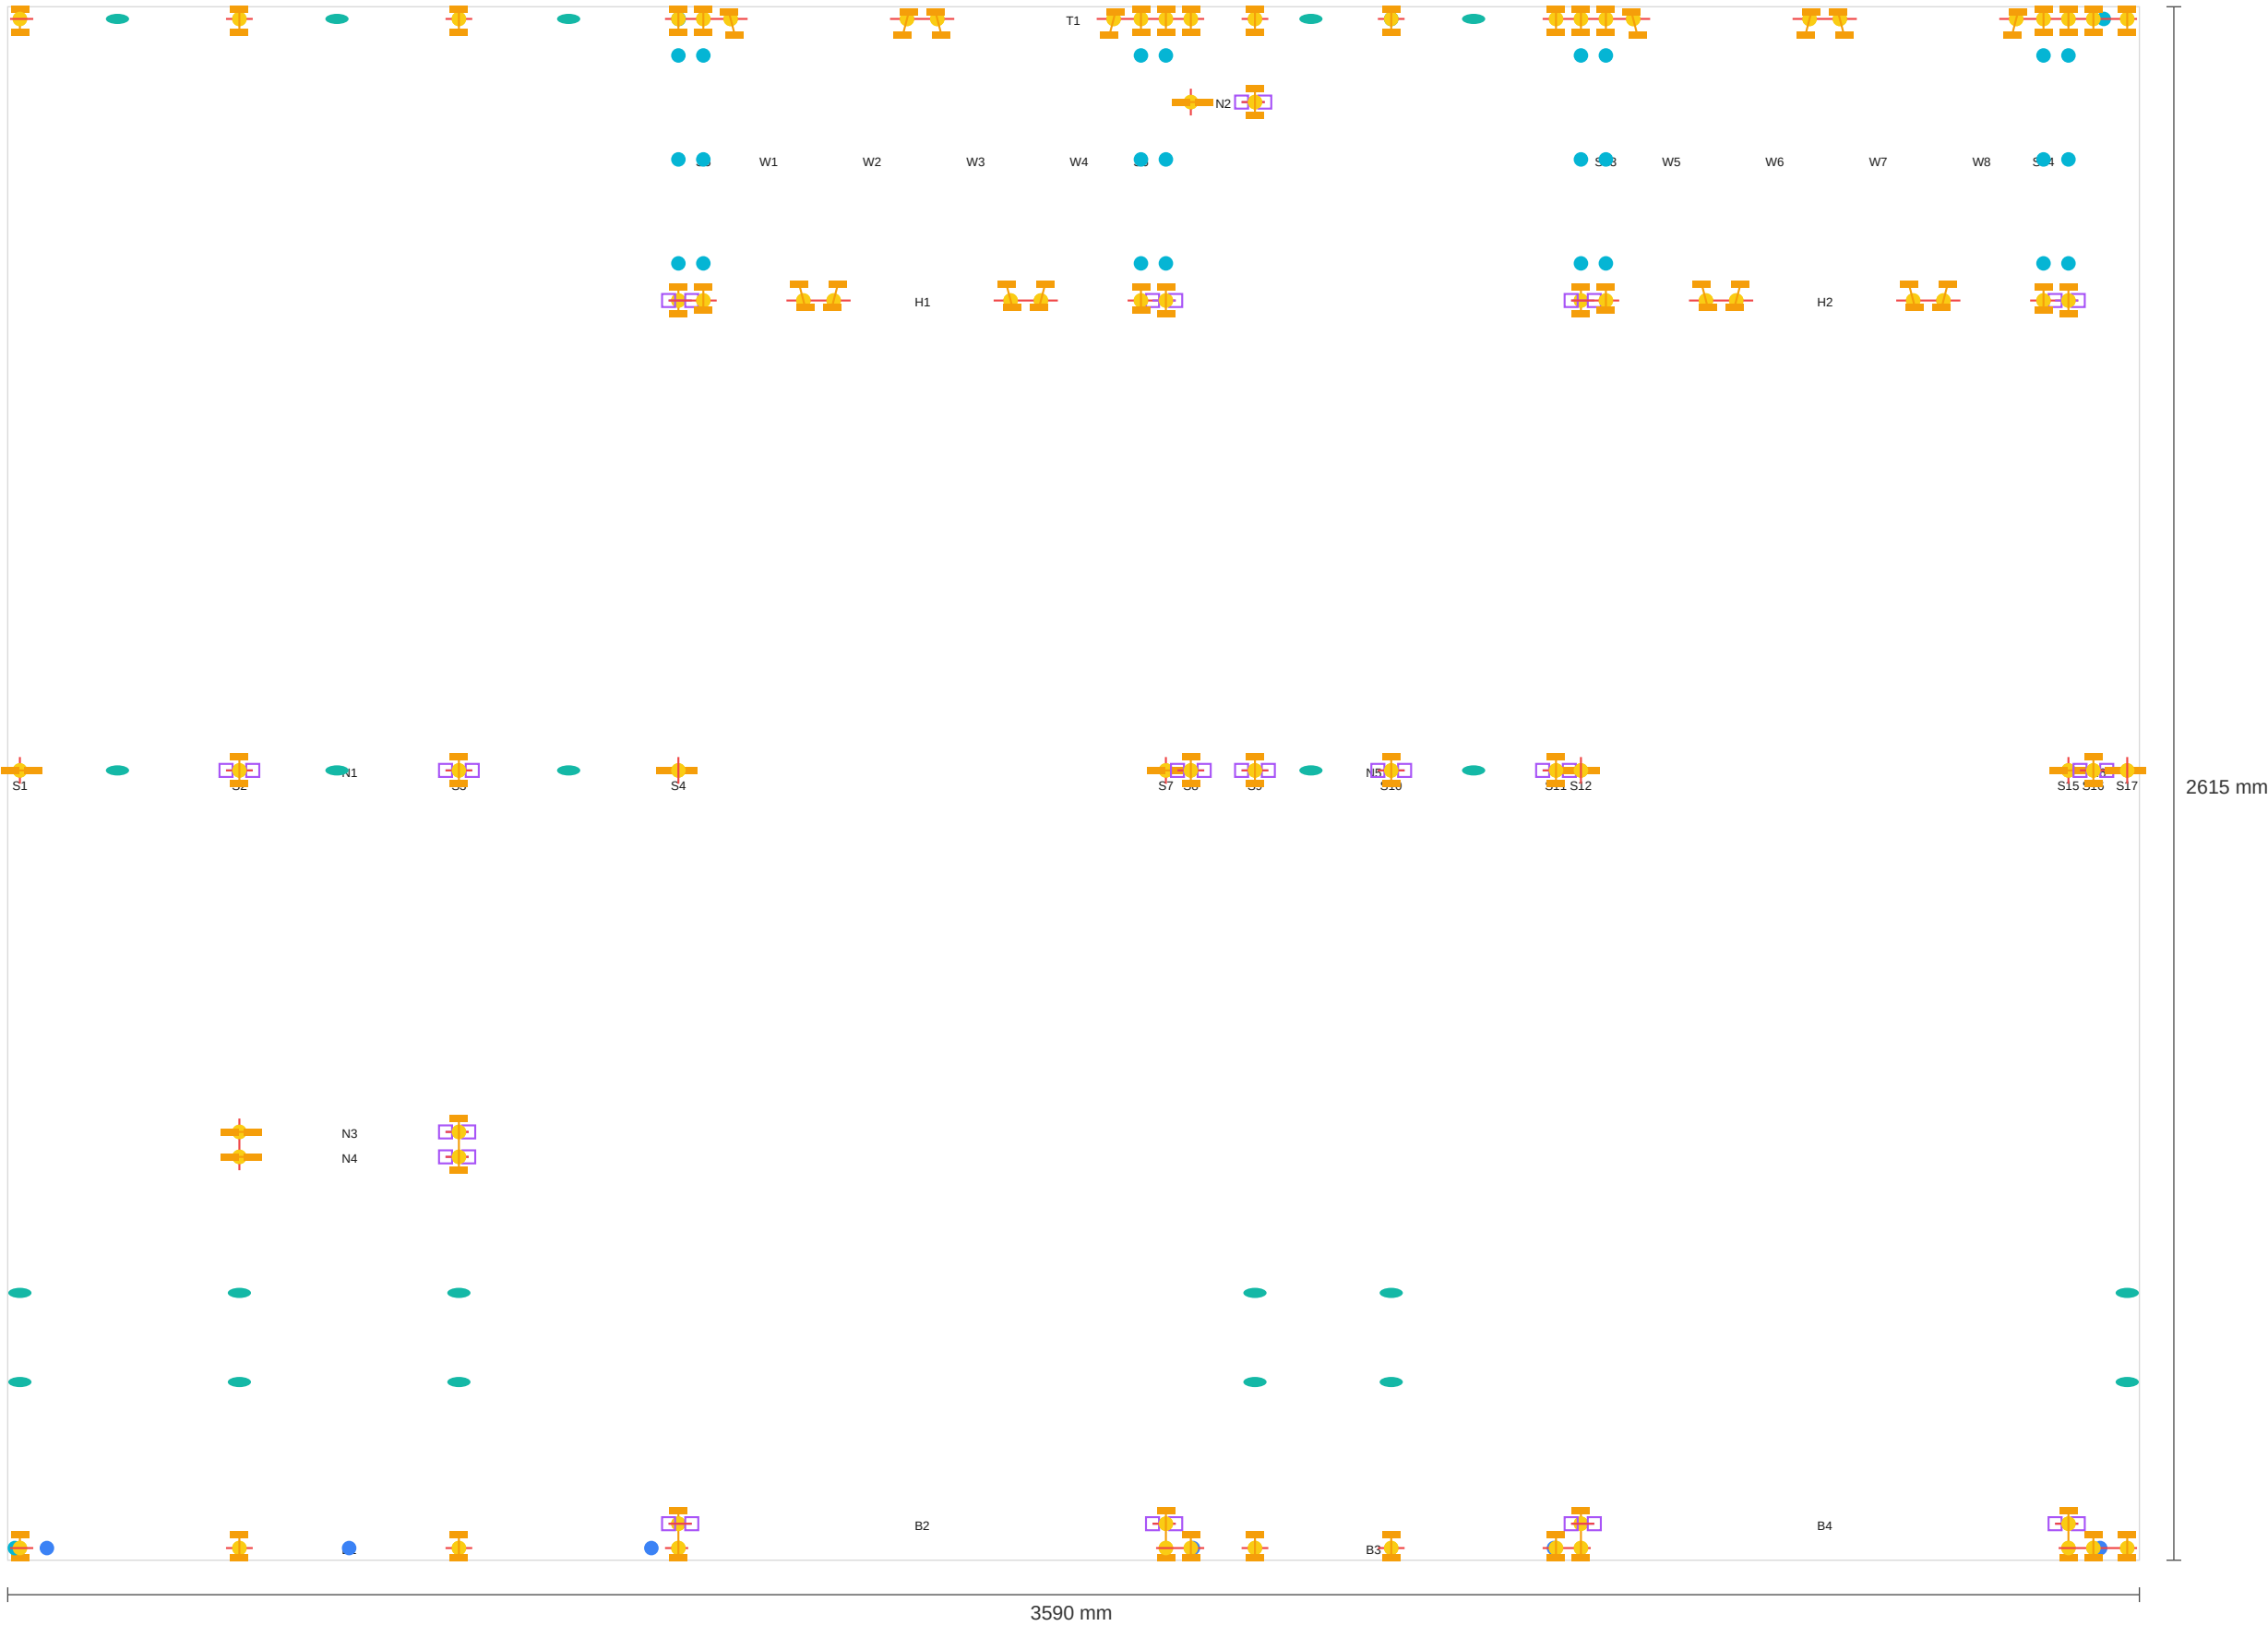

Frame: L26
 Plan: PK4-GF-LBW-70.075
 Length: 1.880 m Height: 2.615 m Weight: 30.4 kg

Project: HG260017#1-1 LOT 925 LOT 925 (42)
 Job: HG260017 Date: 2026-03-05
 STUNNING CRESCENT NARANGBA

HYTEK

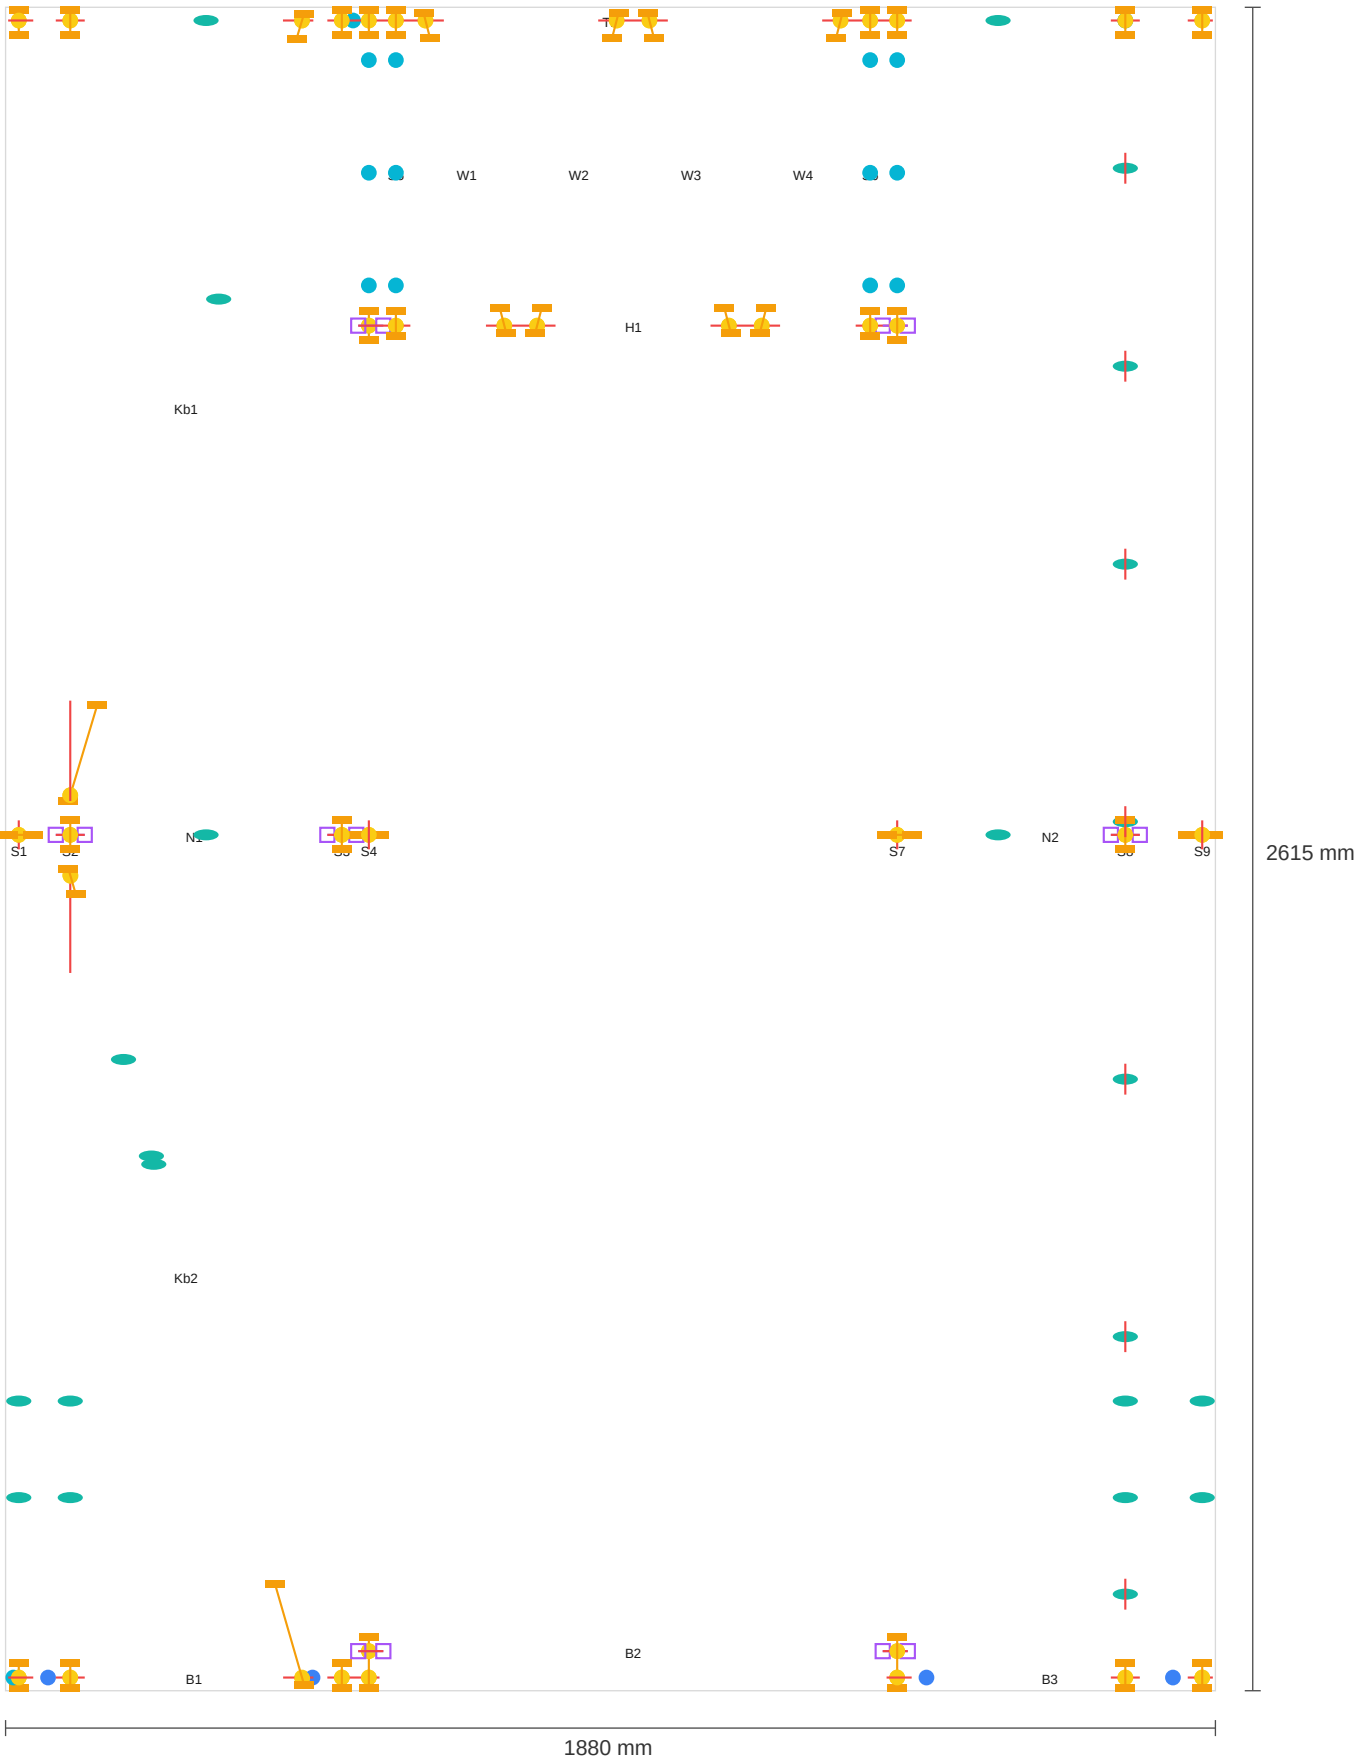


Frame: L33

Plan: PK4-GF-LBW-70.075
Length: 0.400 m Height: 2.604 m Weight: 11.0 kg

Project: HG260017#1-1 LOT 925 LOT 925 (42)
Job: HG260017 Date: 2026-03-05
STUNNING CRESCENT NARANGBA

HYTEK

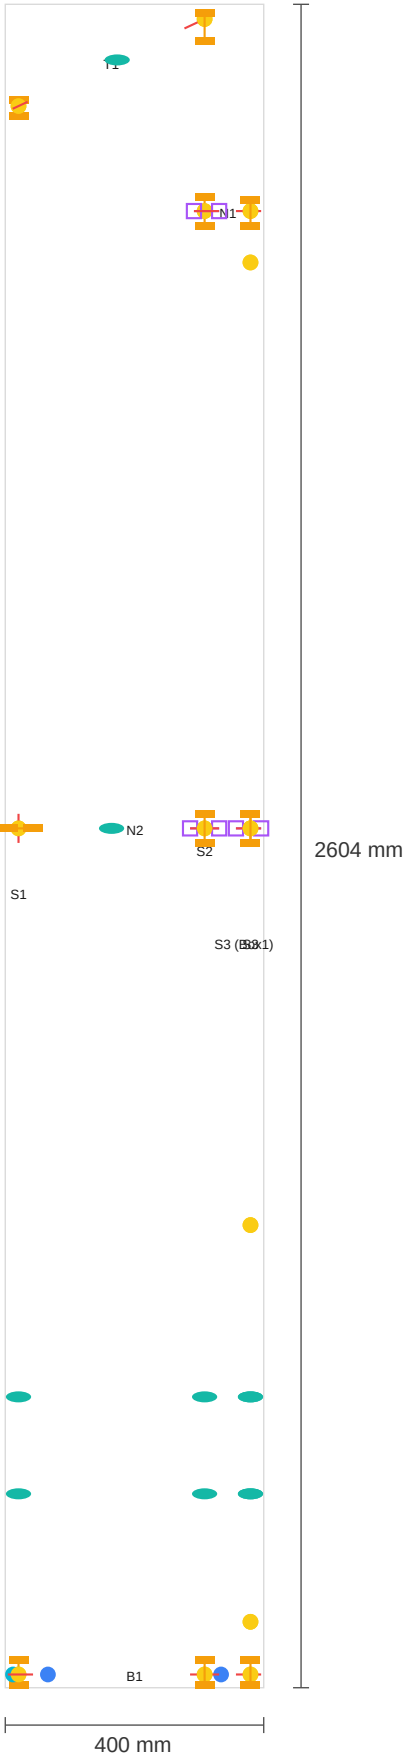

Length: 0.400 m Height: 2.604 m Weight: 11.0 kg

STUNNING CRESCENT NARANGBA


[illegible]

Frame: L31

Plan: PK4-GF-LBW-70.075
Length: 0.400 m Height: 2.604 m Weight: 11.0 kg

Project: HG260017#1-1 LOT 925 LOT 925 (42)
Job: HG260017 Date: 2026-03-05
STUNNING CRESCENT NARANGBA

HYTEK

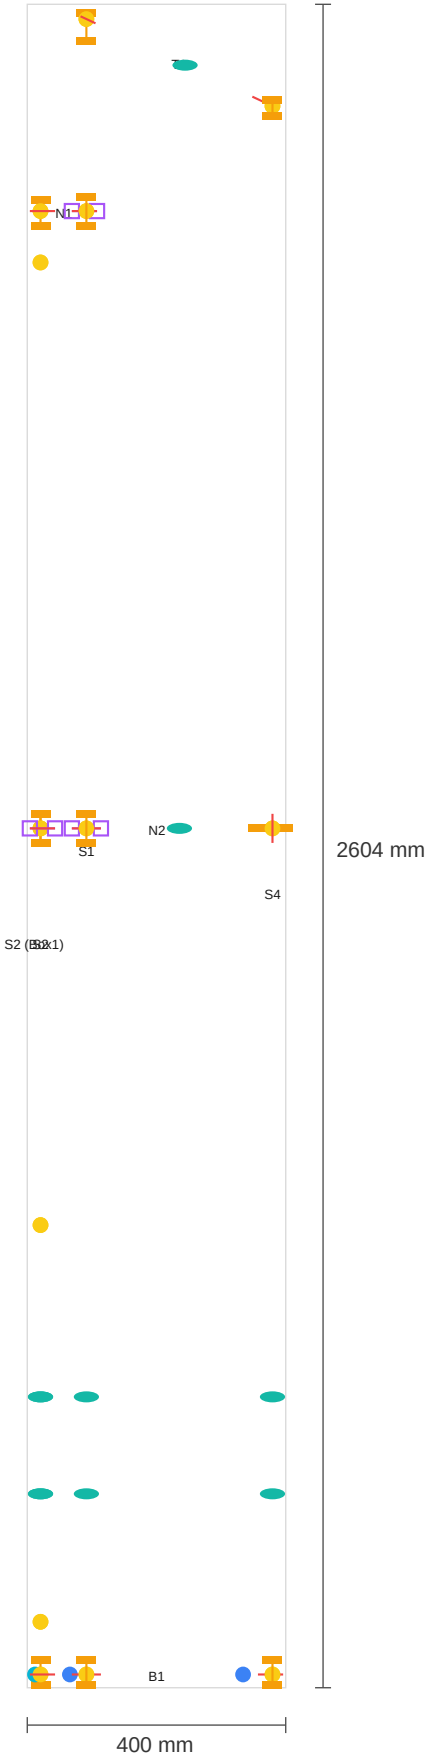

Frame: L25

Plan: PK4-GF-LBW-70.075
Length: 2.842 m Height: 2.615 m Weight: 36.1 kg

Project: HG260017#1-1 LOT 925 LOT 925 (42)
Job: HG260017 Date: 2026-03-05
STUNNING CRESCENT NARANGBA

HYTEK

